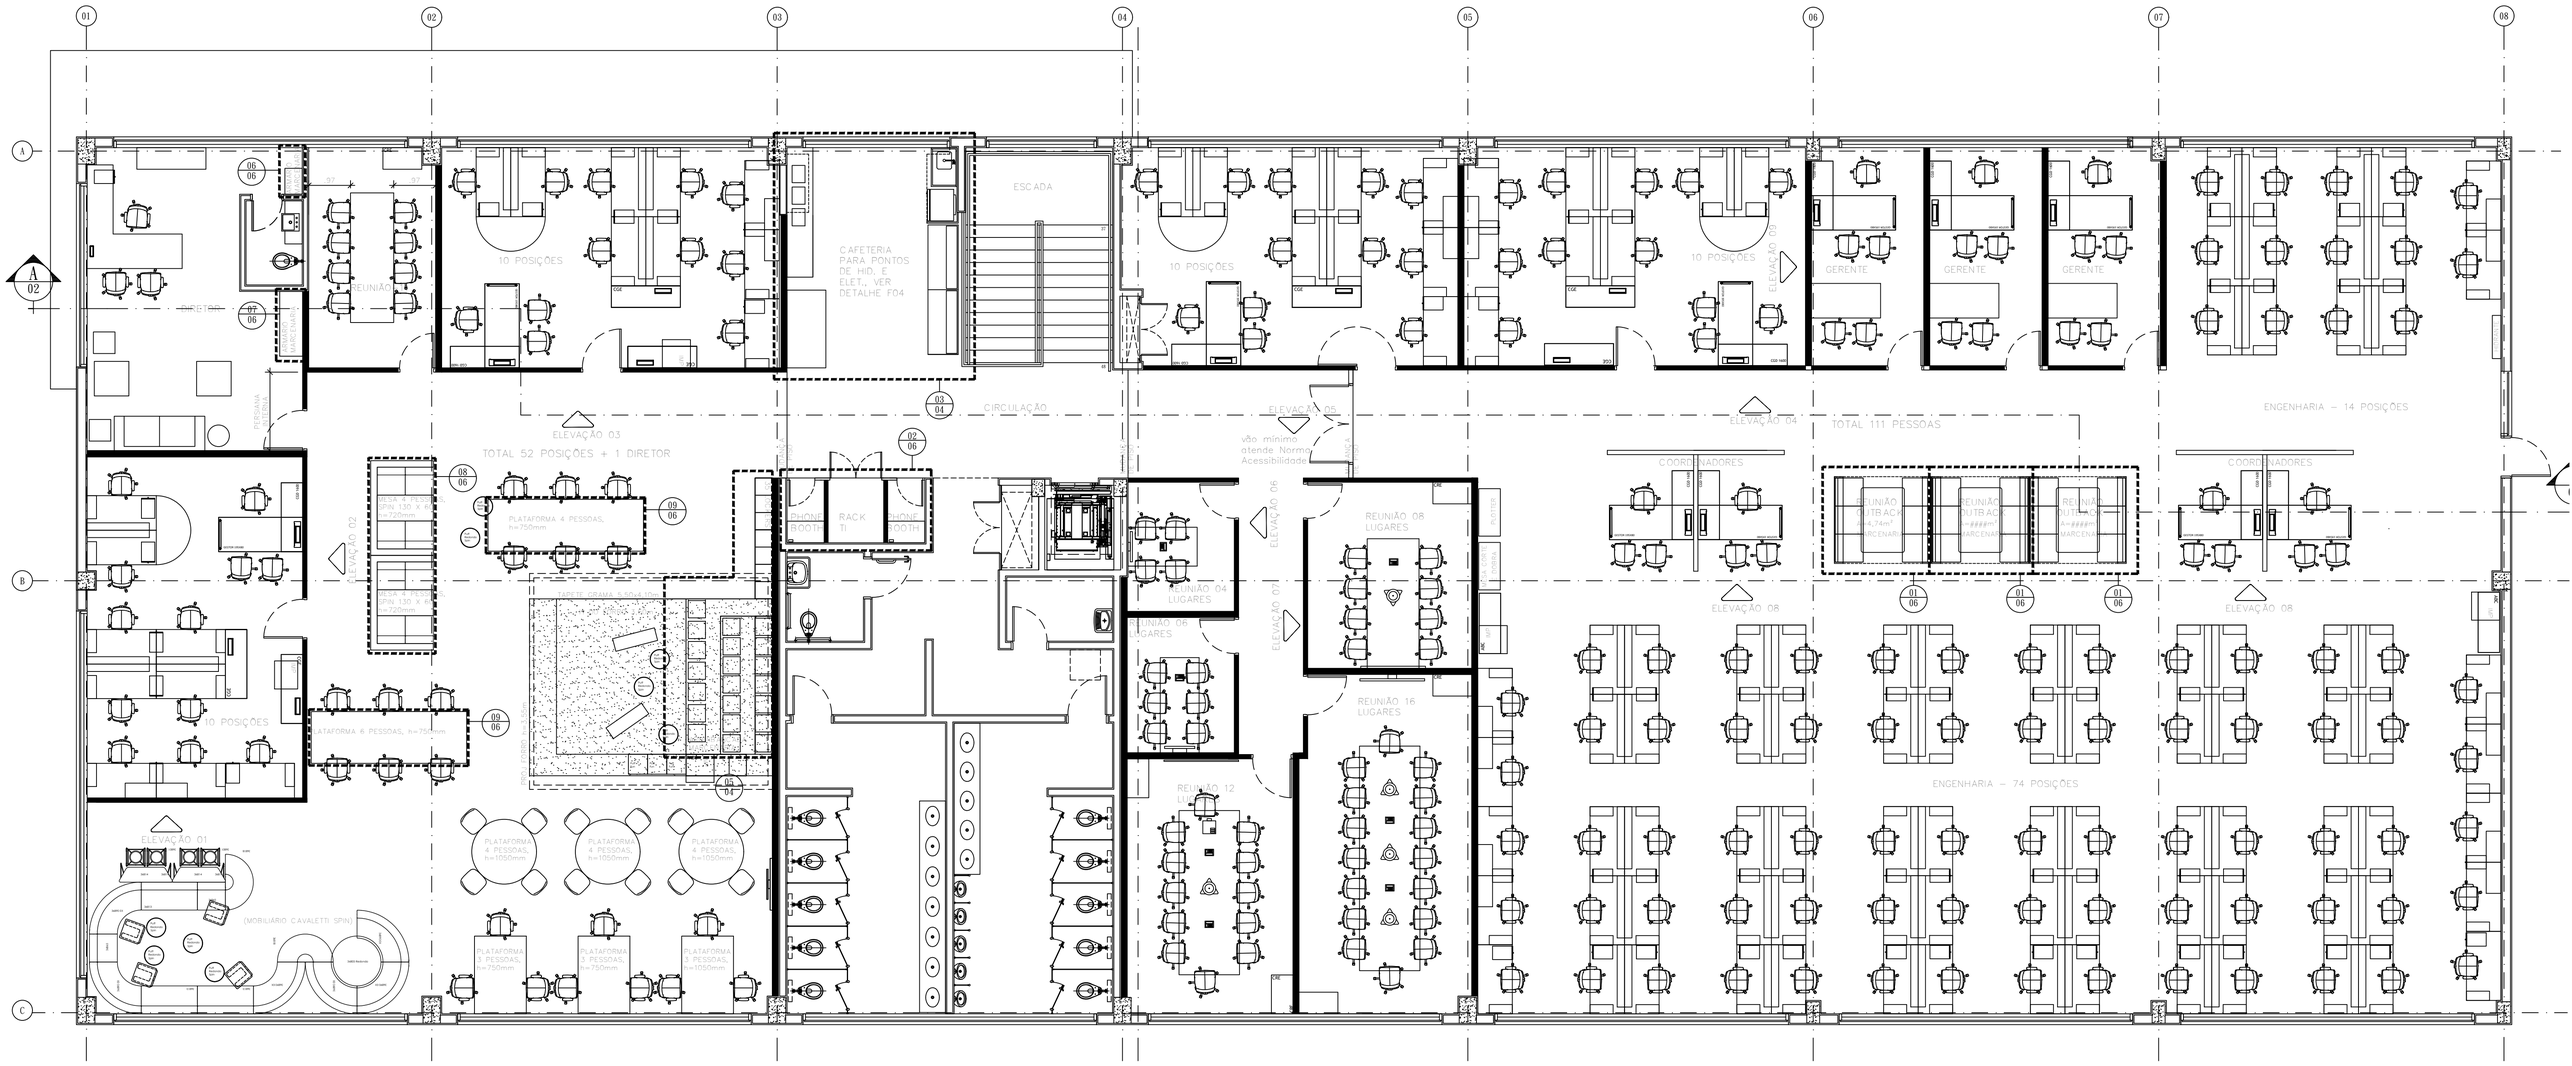
01
02
03
04
05
06
07
08
A
B
C
DIRETOR
PERSIANA
REUNIÃO
10 POSIÇÕES
CAFETERIA PARA PONTOS DE HID. E ELET., VER DETALHE F04
ESCADA
CIRCULAÇÃO
ELEVAÇÃO 03
TOTAL 52 POSIÇÕES + 1 DIRETOR
ELEVAÇÃO 05
vão mínimo atende Norma Acessibilidade
ELEVAÇÃO 04
TOTAL 111 PESSOAS
GERENTE
ENGENHARIA – 14 POSIÇÕES
COORDENADORES
REUNIÃO INTRAÇÃO
ELEVAÇÃO 08
ELEVAÇÃO 02
PLATAFORMA 4 PESSOAS, h=750mm
TAPETE GRAMA 5,50x4,10m
PHONE BOOTH
RACK TI
REUNIÃO 04 LUGARES
REUNIÃO 08 LUGARES
REUNIÃO 16 LUGARES
ELEVAÇÃO 06
ELEVAÇÃO 07
ENGENHARIA – 74 POSIÇÕES
ELEVAÇÃO 01
(MOBILIÁRIO CAVALETTI SPIN)
PLATAFORMA 4 PESSOAS, h=1050mm
PLATAFORMA 3 PESSOAS, h=750mm